


P R E S J E K 1 - 1

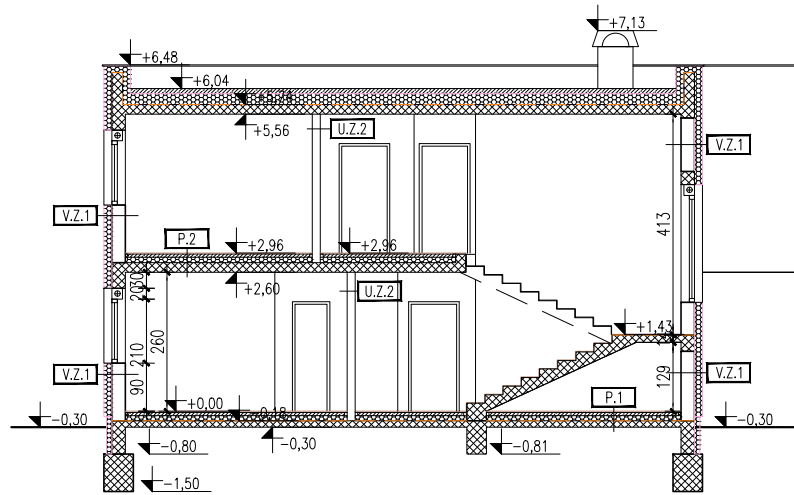

- VZ1 – tankoslojna fasadna žbuka
 - toplotnska izolacija 10 cm
 - blok opeka 25 cm
 - završna zidna obloga

- UZ1 - završna zidna obloga
- blok opeka 25 cm
- završna zidna obloga


- UZ2 - završna zidna obloga
- gipskartonska ploča 1,25 cm
 - nosači za ploče 13,5 cm
 - gipskartonska ploča 1,25 cm
 - završna zidna obloga

- K1 - beton za pad 10 cm
- PVC folija
- toplotna izolacija XPS 20 cm
- hidroizolacija
- AB krovna konstrukcija 18 cm
- završna obloga podgleda

- | | |
|-------------------------|-------|
| P1 - parket | 2 cm |
| - cementni estrih | 6 cm |
| - toplotna izolacija | 10 cm |
| - hidroizolacija | 1 cm |
| - AB podna konstrukcija | 12 cm |
| - nabijeni šljunak | 30 cm |

- | | |
|---------------------------|-------|
| P2 – parket | 2 cm |
| - cementni estrih | 6 cm |
| - toplotinska izolacija | 10 cm |
| - AB stropna konstrukcija | 18 cm |
| - završna obloga podgleda | |

P R E S J E K 2 - 2

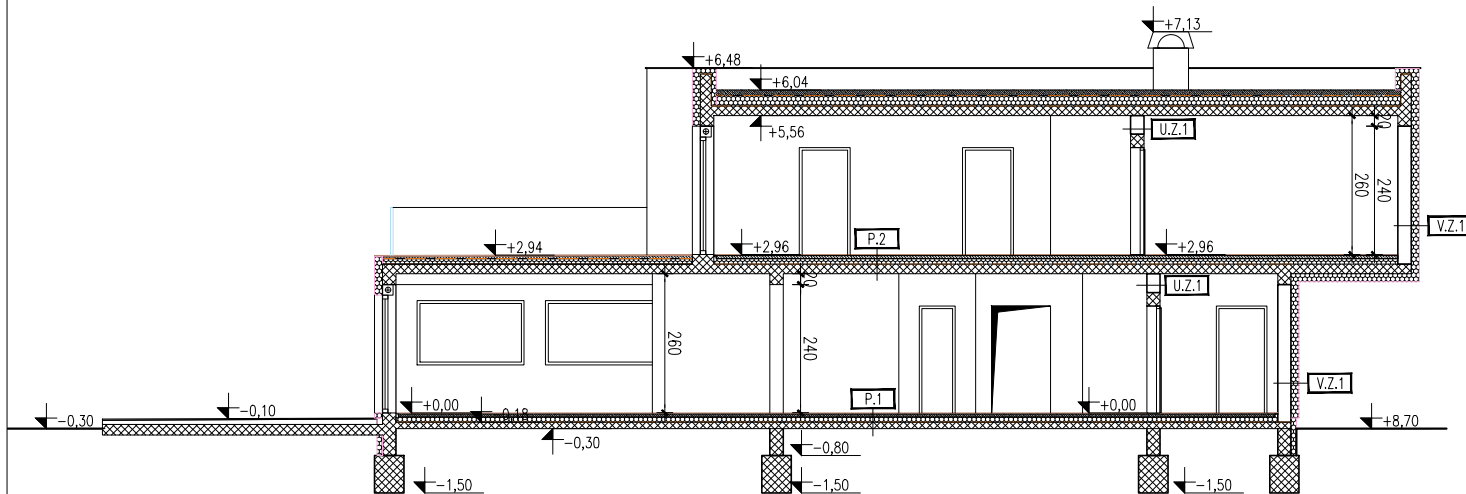

O B I T E L J S K A K U Ć A D R E M P E T I Ć															
T	L	O	C	R	T	P	R	I	Z	E	M	L	J	A	1:100
M A R T A D R E M P E T I Ć															LIST 6